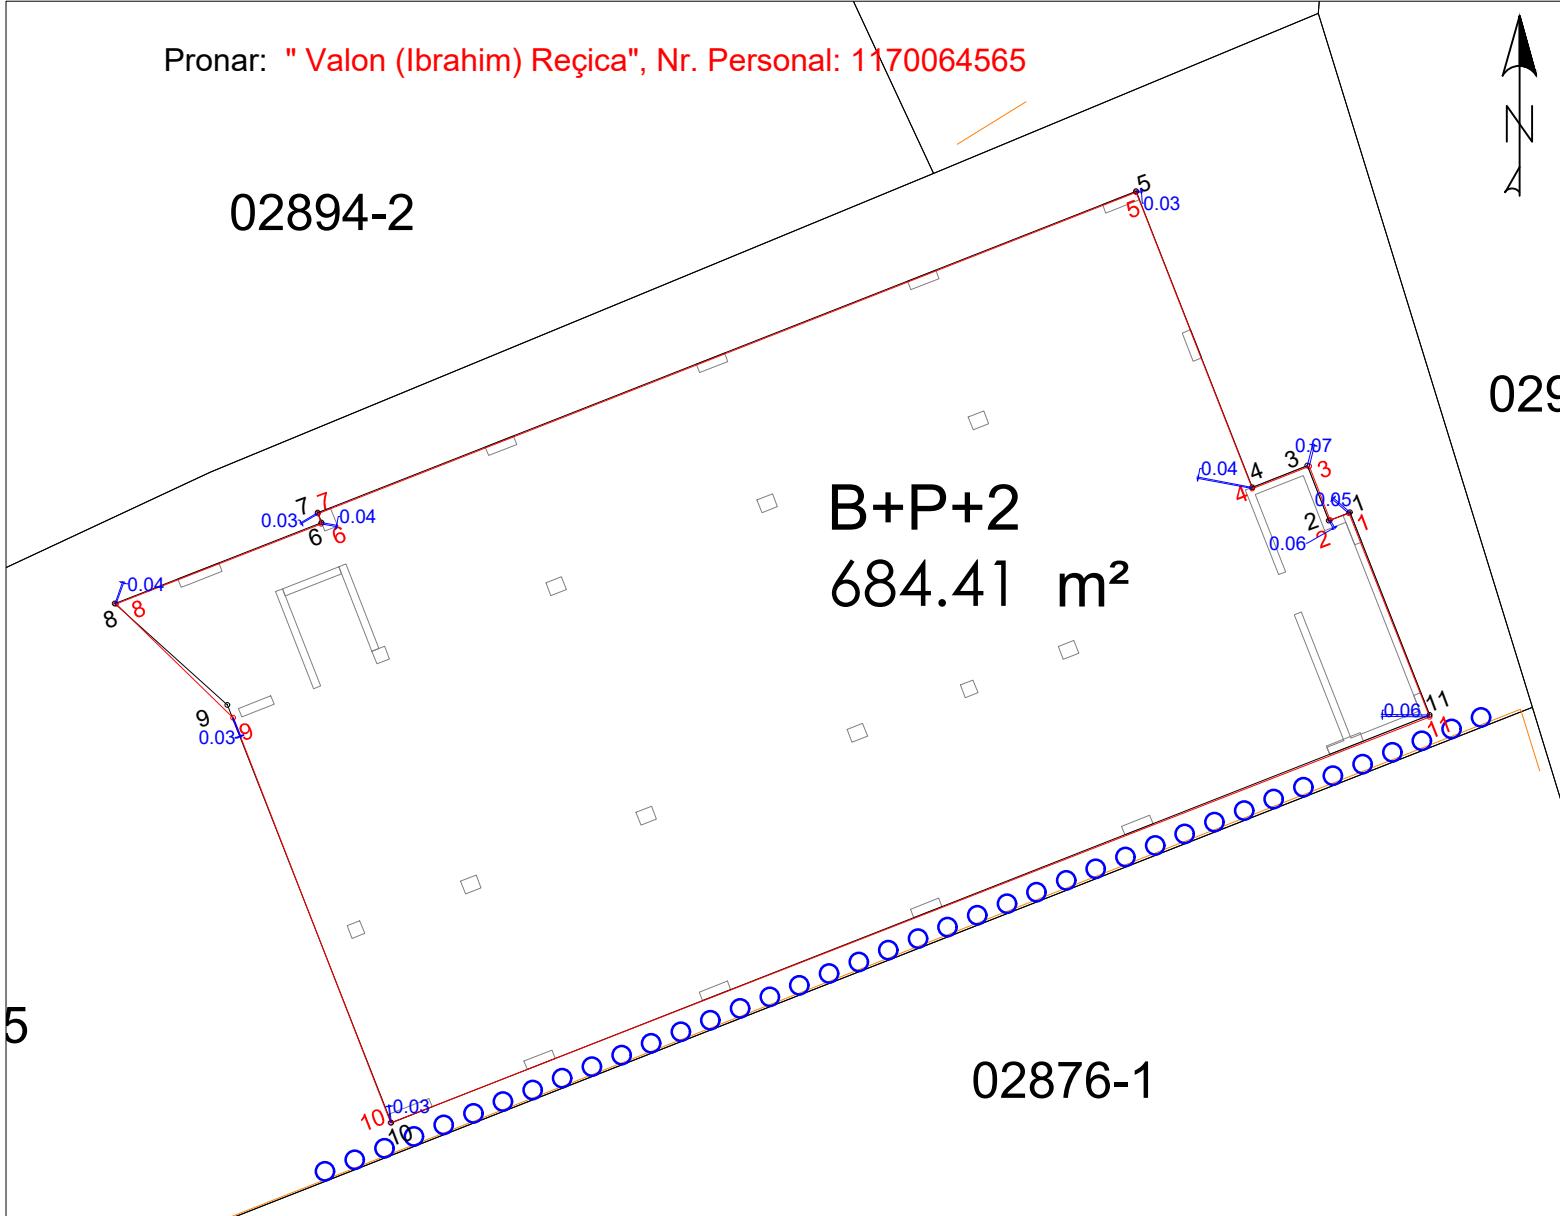


Zyra kadastrale / Opštinska katastarska kancelarija: FerizajNr. i njësisë kadastrale / Br. katastarske jedinice : 00066-25Zona kadastrale / Katastarska zona: Ferizaj

Numri i lëndës / Broj predmeta:

Lloji i njësisë kadastrale / Vrsta katastarske jedinice : Situacion objektitShkalla e zvoglimit / Razmera plana : 1:250**Republika e Kosovës****Republika Kosova-Republic of Kosovo****Qeveria -Vlada-Government****Ministria e Mjedisit dhe Planifikimit Hapësinor /Ministarstvo Sredine i Prostornog Planiranja/Ministry of Environment and Spatial Planning****AGJENCIA KADASTRALE E KOSOVËS/KATASTARSKA AGENCIJA KOSOVA/KOSOVA CADASTRAL AGENCY**Pronar: "Valon (Ibrahim) Reçica", Nr. Personal: **1170064565****02894-2****029****B+P+2  
684.41 m<sup>2</sup>**

Koordinatat e projektuara të përdheses

| Nr | Y           | X           | H     | Kodi     | Përshkrimi      | Burimi |
|----|-------------|-------------|-------|----------|-----------------|--------|
| 1  | 7514042.686 | 4693365.334 | 0.000 | Përdhesa | Shtëpi-Ndërtesë | PP     |
| 2  | 7514041.983 | 4693365.059 | 0.000 | Përdhesa | Shtëpi-Ndërtesë | PP     |
| 3  | 7514041.275 | 4693366.876 | 0.000 | Përdhesa | Shtëpi-Ndërtesë | PP     |
| 4  | 7514039.459 | 4693366.163 | 0.000 | Përdhesa | Shtëpi-Ndërtesë | PP     |
| 5  | 7514035.617 | 4693375.949 | 0.000 | Përdhesa | Shtëpi-Ndërtesë | PP     |
| 7  | 7514008.550 | 4693365.322 | 0.000 | Përdhesa | Shtëpi-Ndërtesë | PP     |
| 6  | 7514008.677 | 4693365.000 | 0.000 | Përdhesa | Shtëpi-Ndërtesë | PP     |
| 8  | 7514001.850 | 4693362.319 | 0.000 | Përdhesa | Shtëpi-Ndërtesë | PP     |
| 9  | 7514005.567 | 4693358.965 | 0.000 | Përdhesa | Shtëpi-Ndërtesë | PP     |
| 10 | 7514010.990 | 4693345.154 | 0.000 | Përdhesa | Shtëpi-Ndërtesë | PP     |
| 11 | 7514045.317 | 4693358.633 | 0.000 | Përdhesa | Shtëpi-Ndërtesë | PP     |

Koordinatat e ekzekutuara të përdheses

| Nr | Y           | X           | H       | Kodi     | Përshkrimi      | Burimi |
|----|-------------|-------------|---------|----------|-----------------|--------|
| 1  | 7514042.655 | 4693365.299 | 619.176 | Përdhesa | Shtëpi-Ndërtesë | PM     |
| 2  | 7514042.031 | 4693365.087 | 619.189 | Përdhesa | Shtëpi-Ndërtesë | PM     |
| 3  | 7514041.338 | 4693366.860 | 619.184 | Përdhesa | Shtëpi-Ndërtesë | PM     |
| 4  | 7514039.452 | 4693366.124 | 619.175 | Përdhesa | Shtëpi-Ndërtesë | PM     |
| 5  | 7514035.619 | 4693375.917 | 619.199 | Përdhesa | Shtëpi-Ndërtesë | PM     |
| 6  | 7514008.669 | 4693364.956 | 619.173 | Përdhesa | Shtëpi-Ndërtesë | PM     |
| 7  | 7514008.568 | 4693365.292 | 619.167 | Përdhesa | Shtëpi-Ndërtesë | PM     |
| 8  | 7514001.886 | 4693362.306 | 619.152 | Përdhesa | Shtëpi-Ndërtesë | PM     |
| 9  | 7514005.766 | 4693358.546 | 619.177 | Përdhesa | Shtëpi-Ndërtesë | PM     |
| 10 | 7514010.963 | 4693345.151 | 619.170 | Përdhesa | Shtëpi-Ndërtesë | PM     |
| 11 | 7514045.316 | 4693358.570 | 619.175 | Përdhesa | Shtëpi-Ndërtesë | PM     |

**LIRIDON SEJDIU**

(emri dhe mbiemri i gjedhet/kompanisë/ ime i prezime gjedeta/ kompanije)

Nr. i licencës / Br. licence: **140**

V.V.

Nënshkrimi / Potpis:

**B1**

Rilevoi / Snimio: \_\_\_\_\_

(emri dhe mbiemri i gjedhet/kompanisë/ ime i prezime gjedeta/ kompanije)

Data e rilevimit / Datum snimanja: **27/11/2025**

Data e aprovimit / Datum usvajanja: \_\_\_\_\_