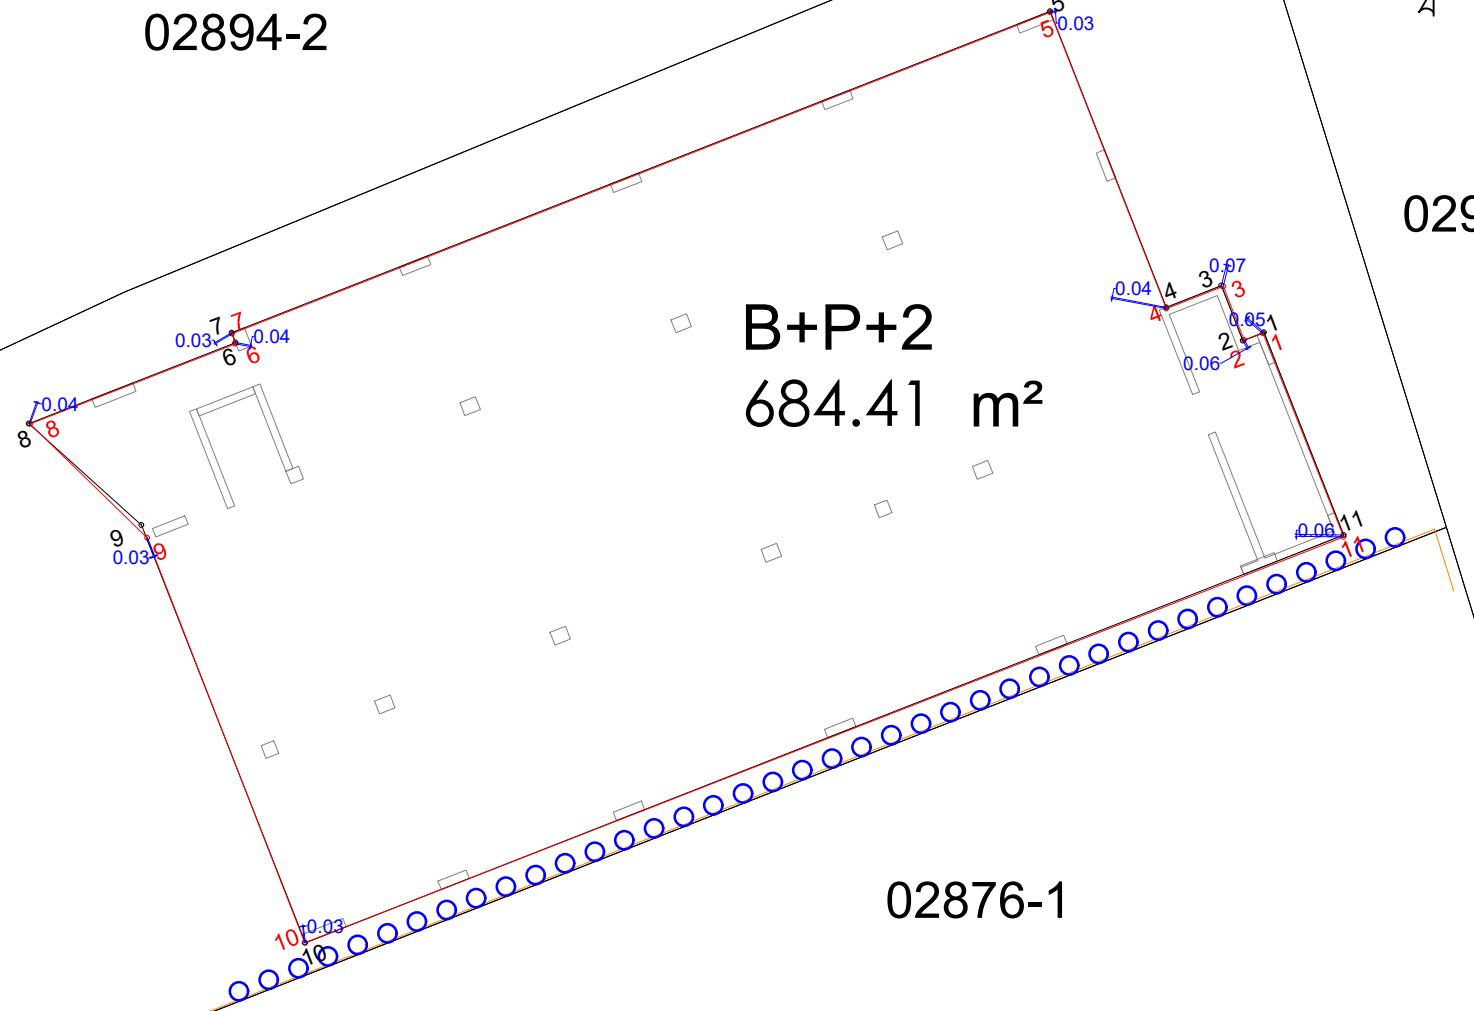


Zyra kadastrale / Opštinska katastarska kancelarija: FerizajNr. i njësisë kadastrale / Br. katastarske jedinice : 00066-25Zona kadastrale / Katastarska zona: Ferizaj

Numri i lëndës / Broj predmeta:

Lloji i njësisë kadastrale / Vrsta katastarske jedinice : Situacion objektitShkalla e zvoglimit / Razmera plana : 1:250**Republika e Kosovës****Republika Kosova-Republic of Kosovo****Qeveria -Vlada-Government****Ministria e Mjedisit dhe Planifikimit Hapësinor /Ministarstvo Sredine i Prostornog Planiranja/Ministry of Environment and Spatial Planning****AGJENCIA KADASTRALE E KOSOVËS/KATASTARSKA AGENCIJA KOSOVA/KOSOVA CADASTRAL AGENCY**Pronar: "Valon (Ibrahim) Reçica", Nr. Personal: **1170064565****02894-2****029****B+P+2
684.41 m²**

Koordinatat e projektuara të përdheses

Nr	Y	X	H	Kodi	Përshkrimi	Burimi
1	7514042.686	4693365.334	0.000	Përdhesa	Shtëpi-Ndërtesë	PP
2	7514041.983	4693365.059	0.000	Përdhesa	Shtëpi-Ndërtesë	PP
3	7514041.275	4693366.876	0.000	Përdhesa	Shtëpi-Ndërtesë	PP
4	7514039.459	4693366.163	0.000	Përdhesa	Shtëpi-Ndërtesë	PP
5	7514035.617	4693375.949	0.000	Përdhesa	Shtëpi-Ndërtesë	PP
7	7514008.550	4693365.322	0.000	Përdhesa	Shtëpi-Ndërtesë	PP
6	7514008.677	4693365.000	0.000	Përdhesa	Shtëpi-Ndërtesë	PP
8	7514001.850	4693362.319	0.000	Përdhesa	Shtëpi-Ndërtesë	PP
9	7514005.567	4693358.965	0.000	Përdhesa	Shtëpi-Ndërtesë	PP
10	7514010.990	4693345.154	0.000	Përdhesa	Shtëpi-Ndërtesë	PP
11	7514045.317	4693358.633	0.000	Përdhesa	Shtëpi-Ndërtesë	PP

Koordinatat e ekzekutuara të përdheses

Nr	Y	X	H	Kodi	Përshkrimi	Burimi
1	7514042.655	4693365.299	619.176	Përdhesa	Shtëpi-Ndërtesë	PM
2	7514042.031	4693365.087	619.189	Përdhesa	Shtëpi-Ndërtesë	PM
3	7514041.338	4693366.860	619.184	Përdhesa	Shtëpi-Ndërtesë	PM
4	7514039.452	4693366.124	619.175	Përdhesa	Shtëpi-Ndërtesë	PM
5	7514035.619	4693375.917	619.199	Përdhesa	Shtëpi-Ndërtesë	PM
6	7514008.669	4693364.956	619.173	Përdhesa	Shtëpi-Ndërtesë	PM
7	7514008.568	4693365.292	619.167	Përdhesa	Shtëpi-Ndërtesë	PM
8	7514001.886	4693362.306	619.152	Përdhesa	Shtëpi-Ndërtesë	PM
9	7514005.766	4693358.546	619.177	Përdhesa	Shtëpi-Ndërtesë	PM
10	7514010.963	4693345.151	619.170	Përdhesa	Shtëpi-Ndërtesë	PM
11	7514045.316	4693358.570	619.175	Përdhesa	Shtëpi-Ndërtesë	PM

Rilevoi / Snimio: **LIRIDON SEJDIU**

(emri dhe mbiemi i gjedhet/kompanisë/ ime i prezime gjedeta/ kompanije)

Nr. i licencës / Br. licence: **140**

V.V.

Nënshkrimi / Potpis:

Përdhesa

Rilevoi / Snimio: _____

(emri dhe mbiemi i gjedhet/kompanisë/ ime i prezime gjedeta/ kompanije)

Data e rilevimit / Datum snimanja: **27/11/2025**

Data e aprovimit / Datum usvajanja: _____